


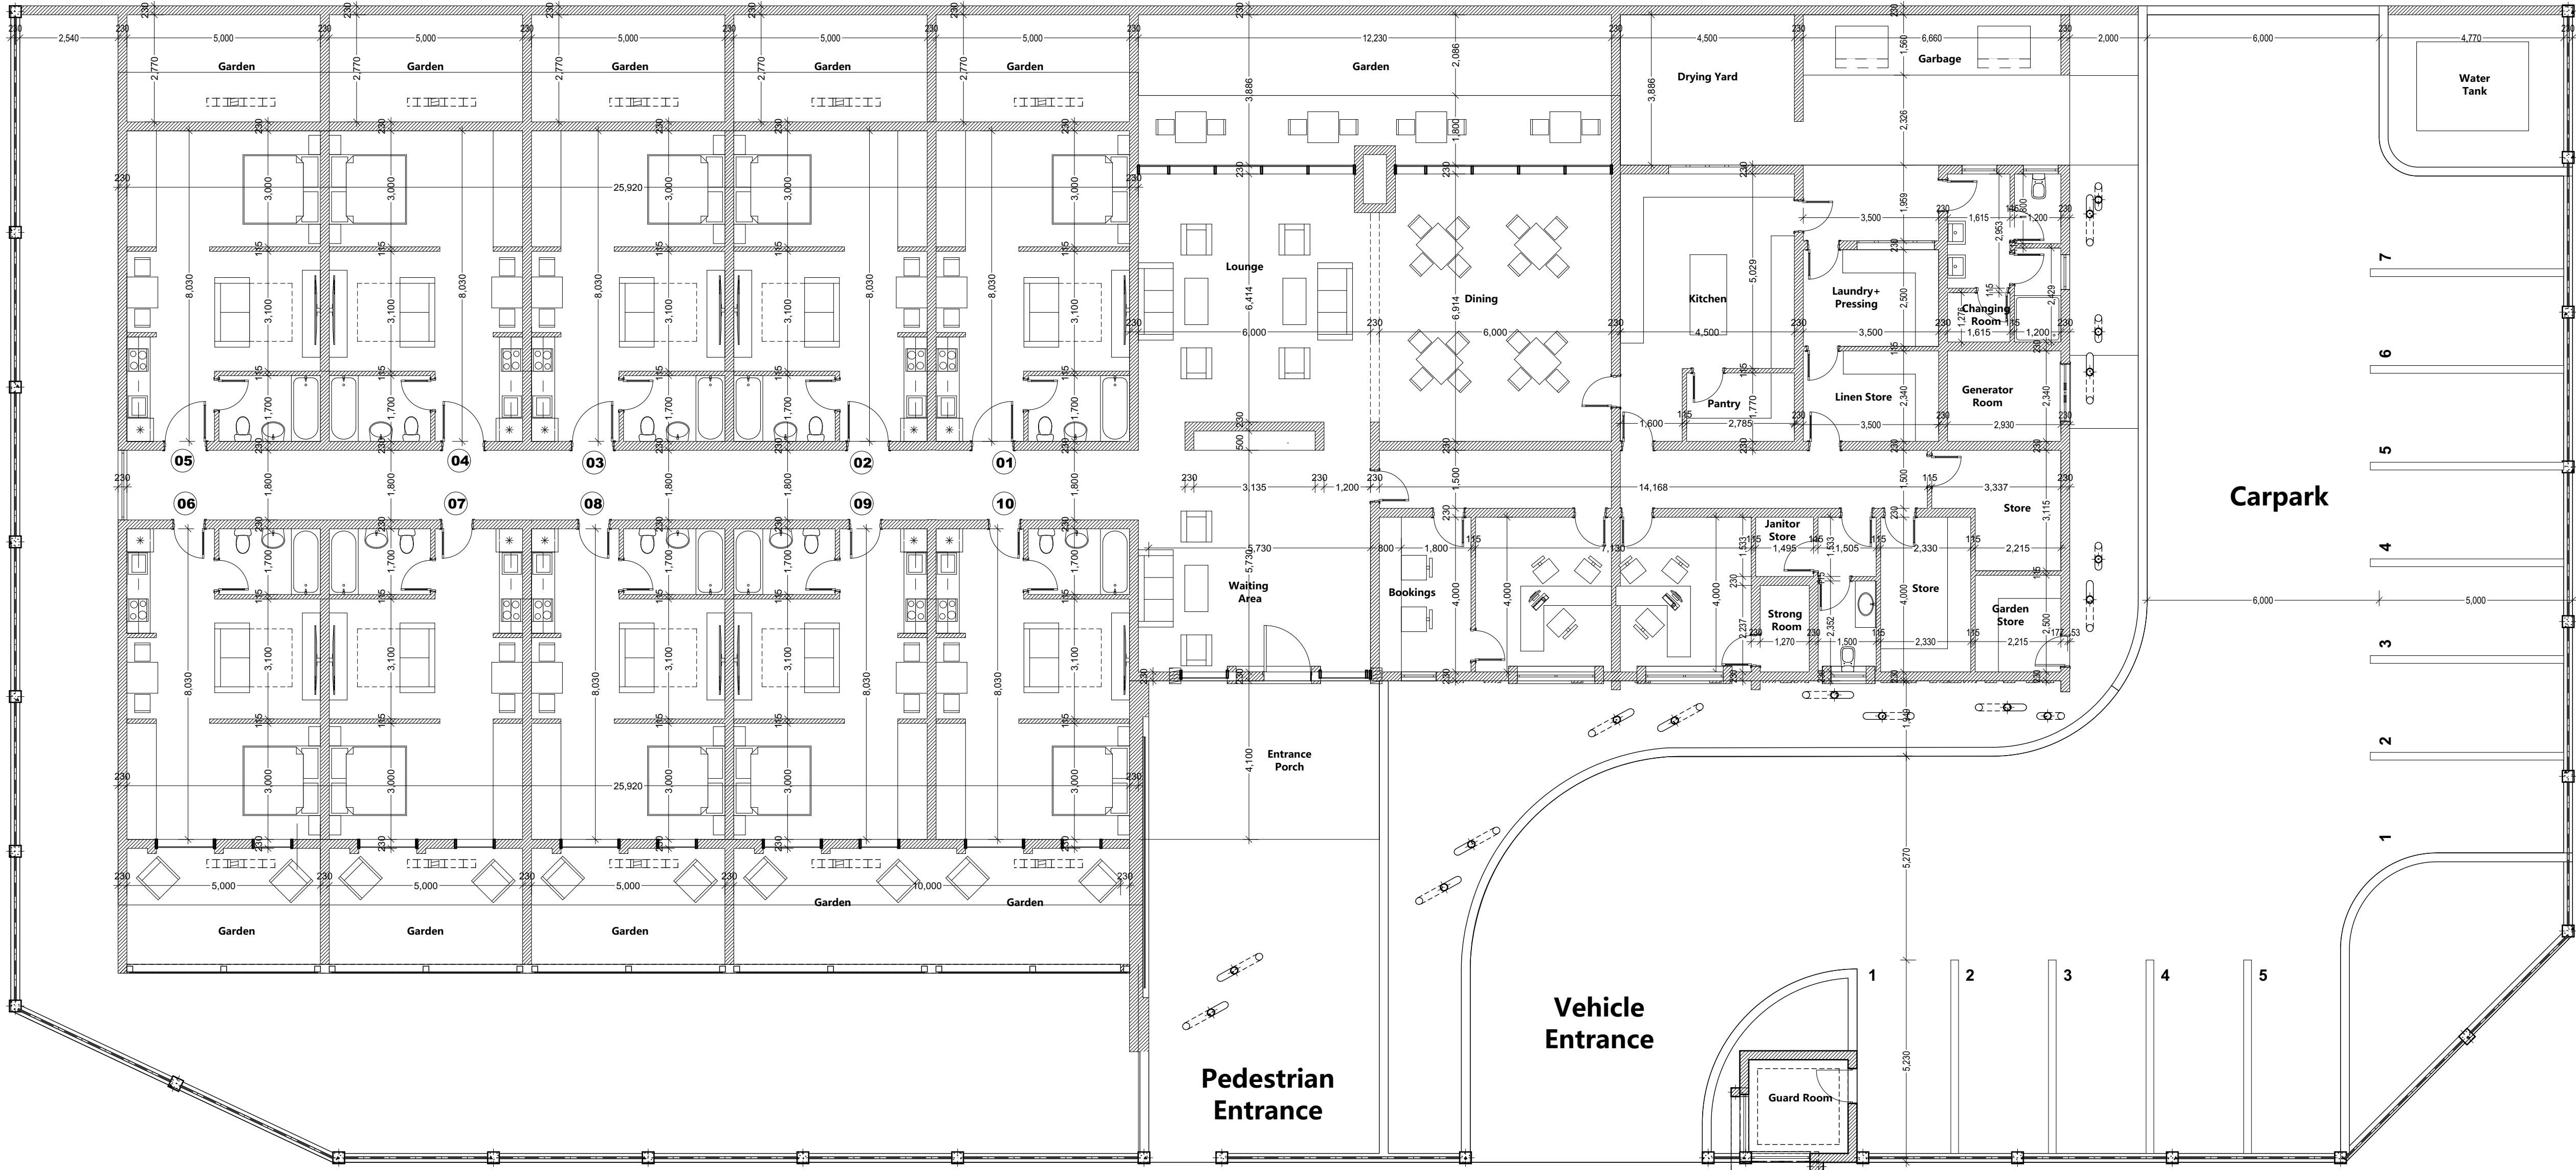


GENERAL NOTES:

- A. FIGURED DIMENSIONS TO BE TAKEN.
- B. THIS DRAWING IS NOT TO BE SCALED.
- C. ALL LEVELS SHOWN ARE FINISHED LEVELS, UNLESS OTHERWISE STATED.
- D. ANY DISCREPANCY MUST BE REPORTED TO THE ARCHITECTS BEFORE THE WORK IS PUT IN HAND.
- E. CONTRACTORS TO SET OUT ONE COURSE OF BRICKWORK AND DOOR AND WINDOW FRAMES IN TYPICAL SECTIONS FOR ARCHITECTS' APPROVAL, BEFORE PUTTING WORK IN HAND.
- F. AIR BRICKS AS INDICATED ON 1:50 PLAN.
- G. WINDOW DRENCHERS ABOVE ALL WINDOWS WITHIN 3M OF FIRE ESCAPE STAIR.

DRAINAGE NOTES:

- A. ALL PLUMBING AND DRAINAGE WORK AND INSTALLATION OF SANITARY FITTINGS TO COMPLY WITH THE NATIONAL BUILDING REGULATIONS.
- B. PROVIDE I.E.'s TO ALL BENDS AND JUNCTIONS WITH SUITABLE MARKERS AT GROUND LEVEL.
- C. MINIMUM FALL TO ALL DRAIN PIPES TO BE 1:40.
- D. PROVIDE APPROVED RESEAL TRAPS TO ALL WASTE FITTINGS, TO COMPLY WITH NATIONAL BUILDING REGULATIONS.
- E. PROVIDE A.E.'s TO FOOT OF ALL SOIL STACKS.
- F. I.E.'s TO WASTE PIPES TO BE FULLY ACCESSIBLE AT ALL TIMES.
- G. ALL WASTE FITTINGS ON THE SINGLE STACK SYSTEM TO HAVE 75mm DEEP-SEAL RESEALING TRAP AND AN APPROVED VENT VALVE WHERE REQUIRED.
- H. DRAINS UNDER BUILDINGS TO BE ADEQUATELY PROTECTED AGAINST LOAD.
- I. PROVIDE ADEQUATE ACCESS TO WASTE AND SOIL PIPES FOR CLEANING, REPAIRS, ETC.

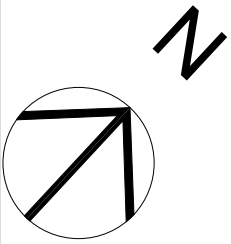

NO.	REVISION	DATE
01		
00		

365
STUDIO
+971526560289

PROJECT TITLE

**PROPOSED HOTEL FOR
MISHECK KALUBA CHONGO**

SITE PLAN, SCHEDULES & SEPTIC TANK

DRAWING

N/02/17	JUL 2017	NITRO
PROJECT NO.	DATE	DRAWN
A1001		01
DRAWING NO.		REVISION

ISSUED FOR

CONSTRUCTION